
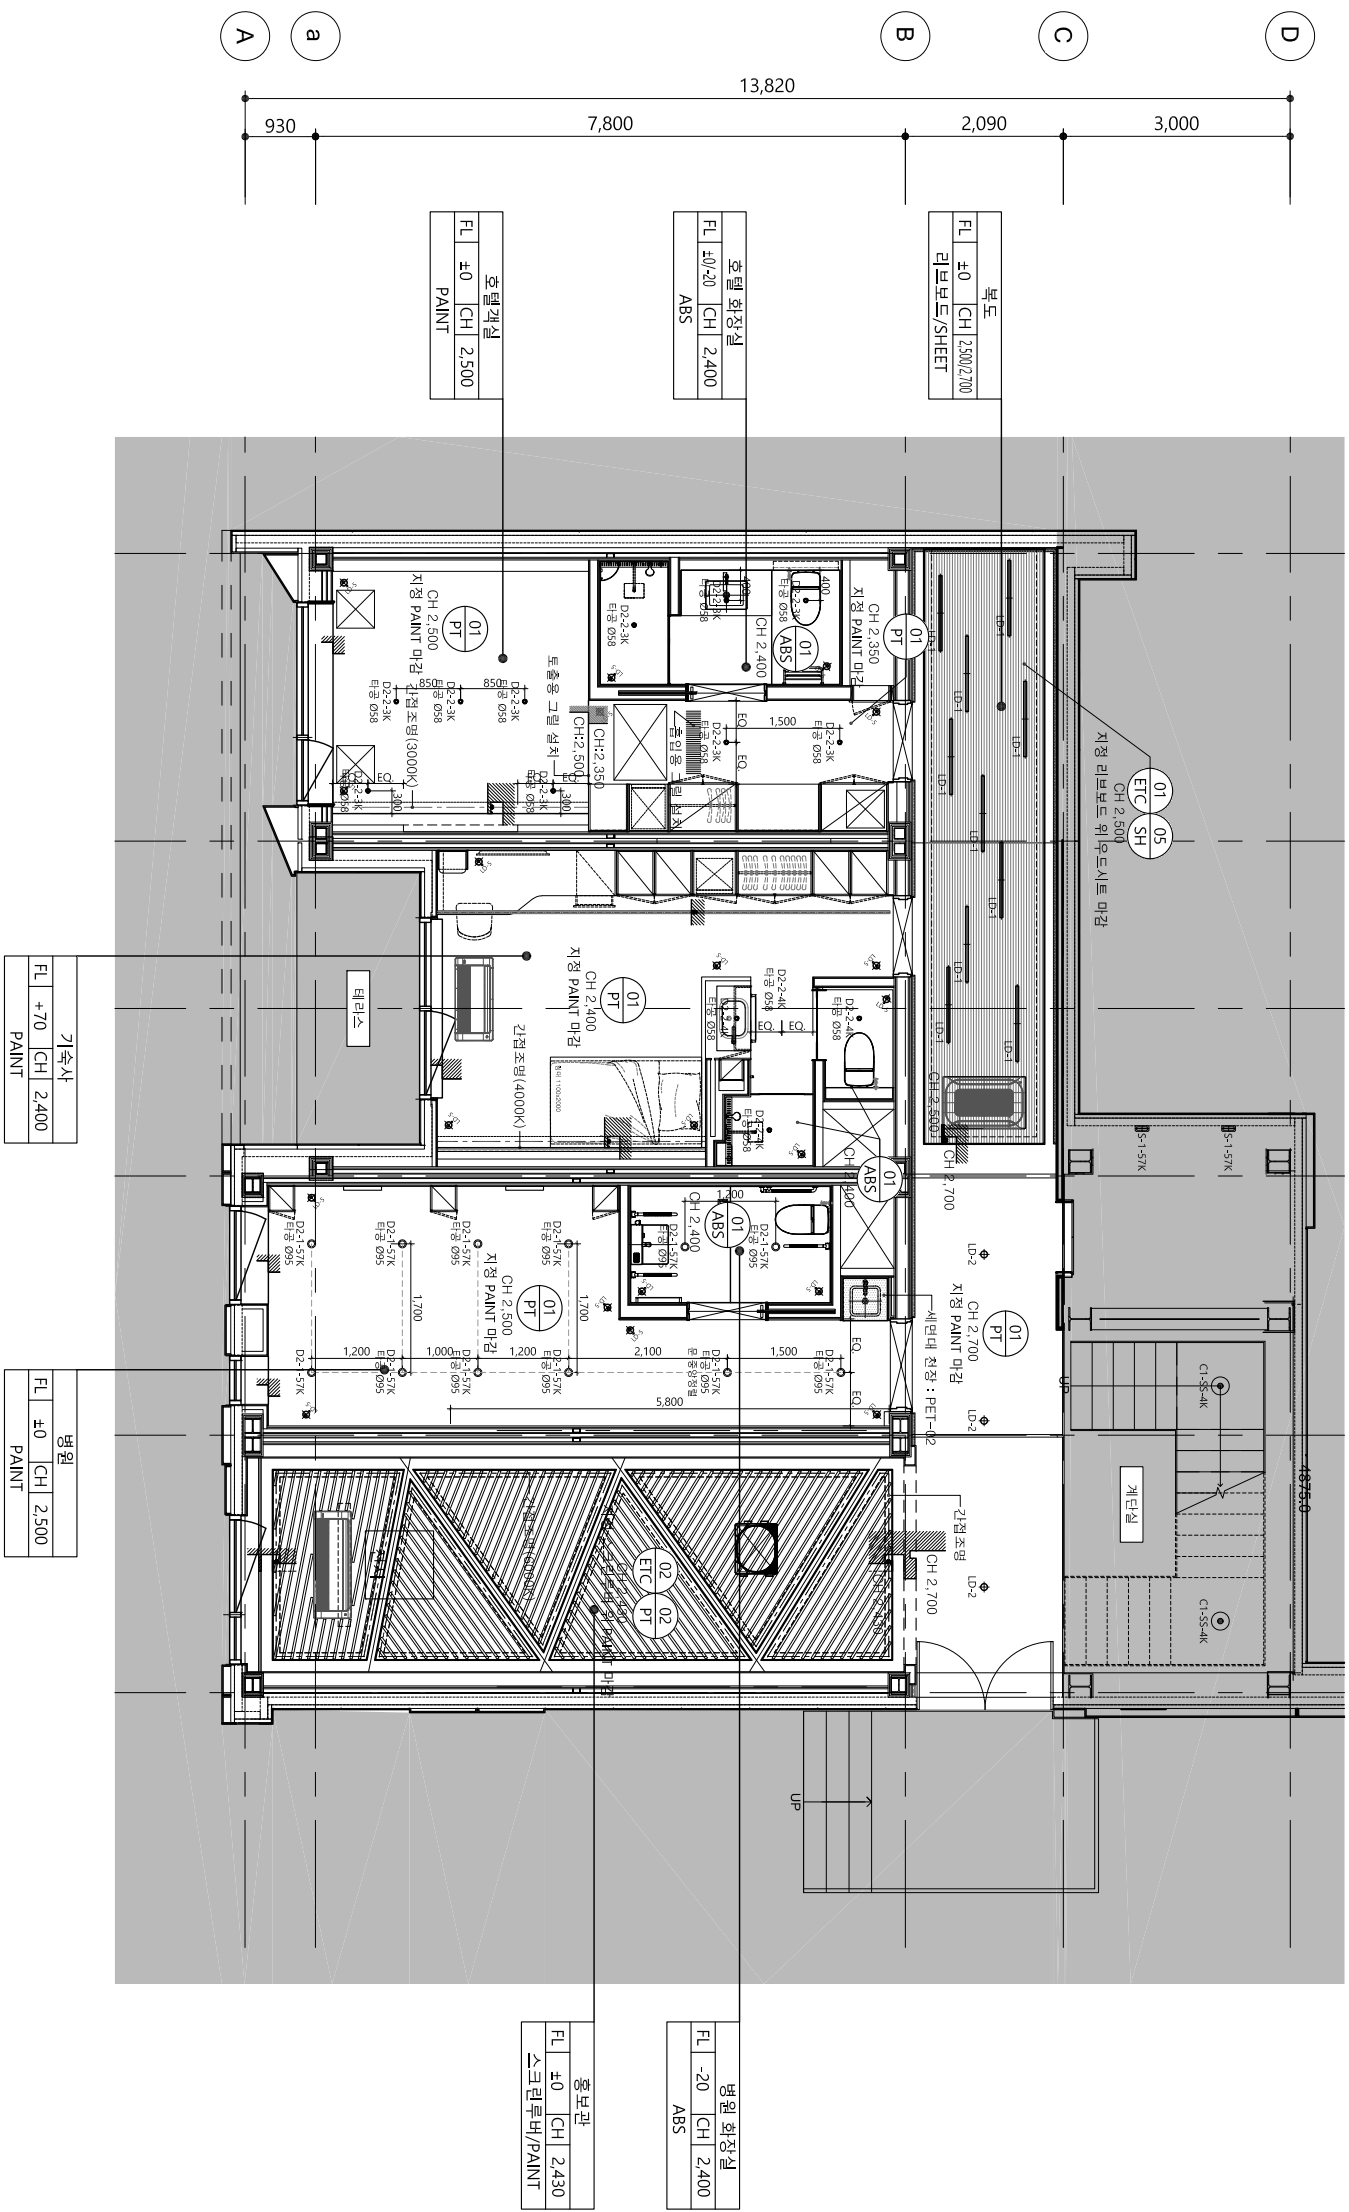


PROJECT TITLE

현대엔지니어링
모듈러주택 테스트베드
인테리어 설계

NOTE

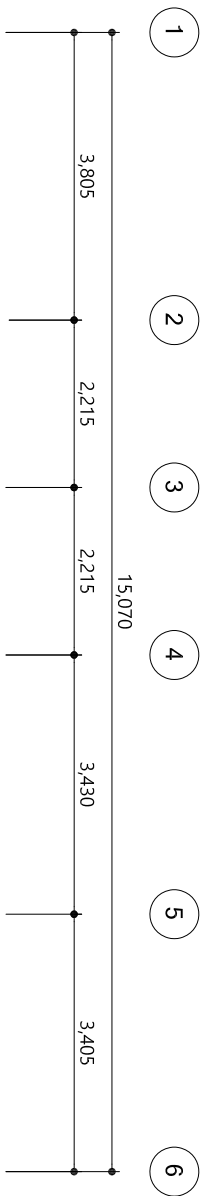

인테리어 영역
건축 영역

FORTE
ARCHITECTURE & INTERIOR

33-1, Bongeunsa-ro 68-gil FORTE B/D
GANGNAM-GU SEOUL, KOREA

DATE 2024.10.

APPROVE

CHECKED BY

DRAWN BY

SCALE	A1	1 / 50
-------	----	--------

A3
1 / 100

DRAFTING TITLE

지상1층 천정도

SHEET NO.

005

DRAWING NO.

P-102

1. 사안 개요

SCALE

A1:1/50, A3:1/100