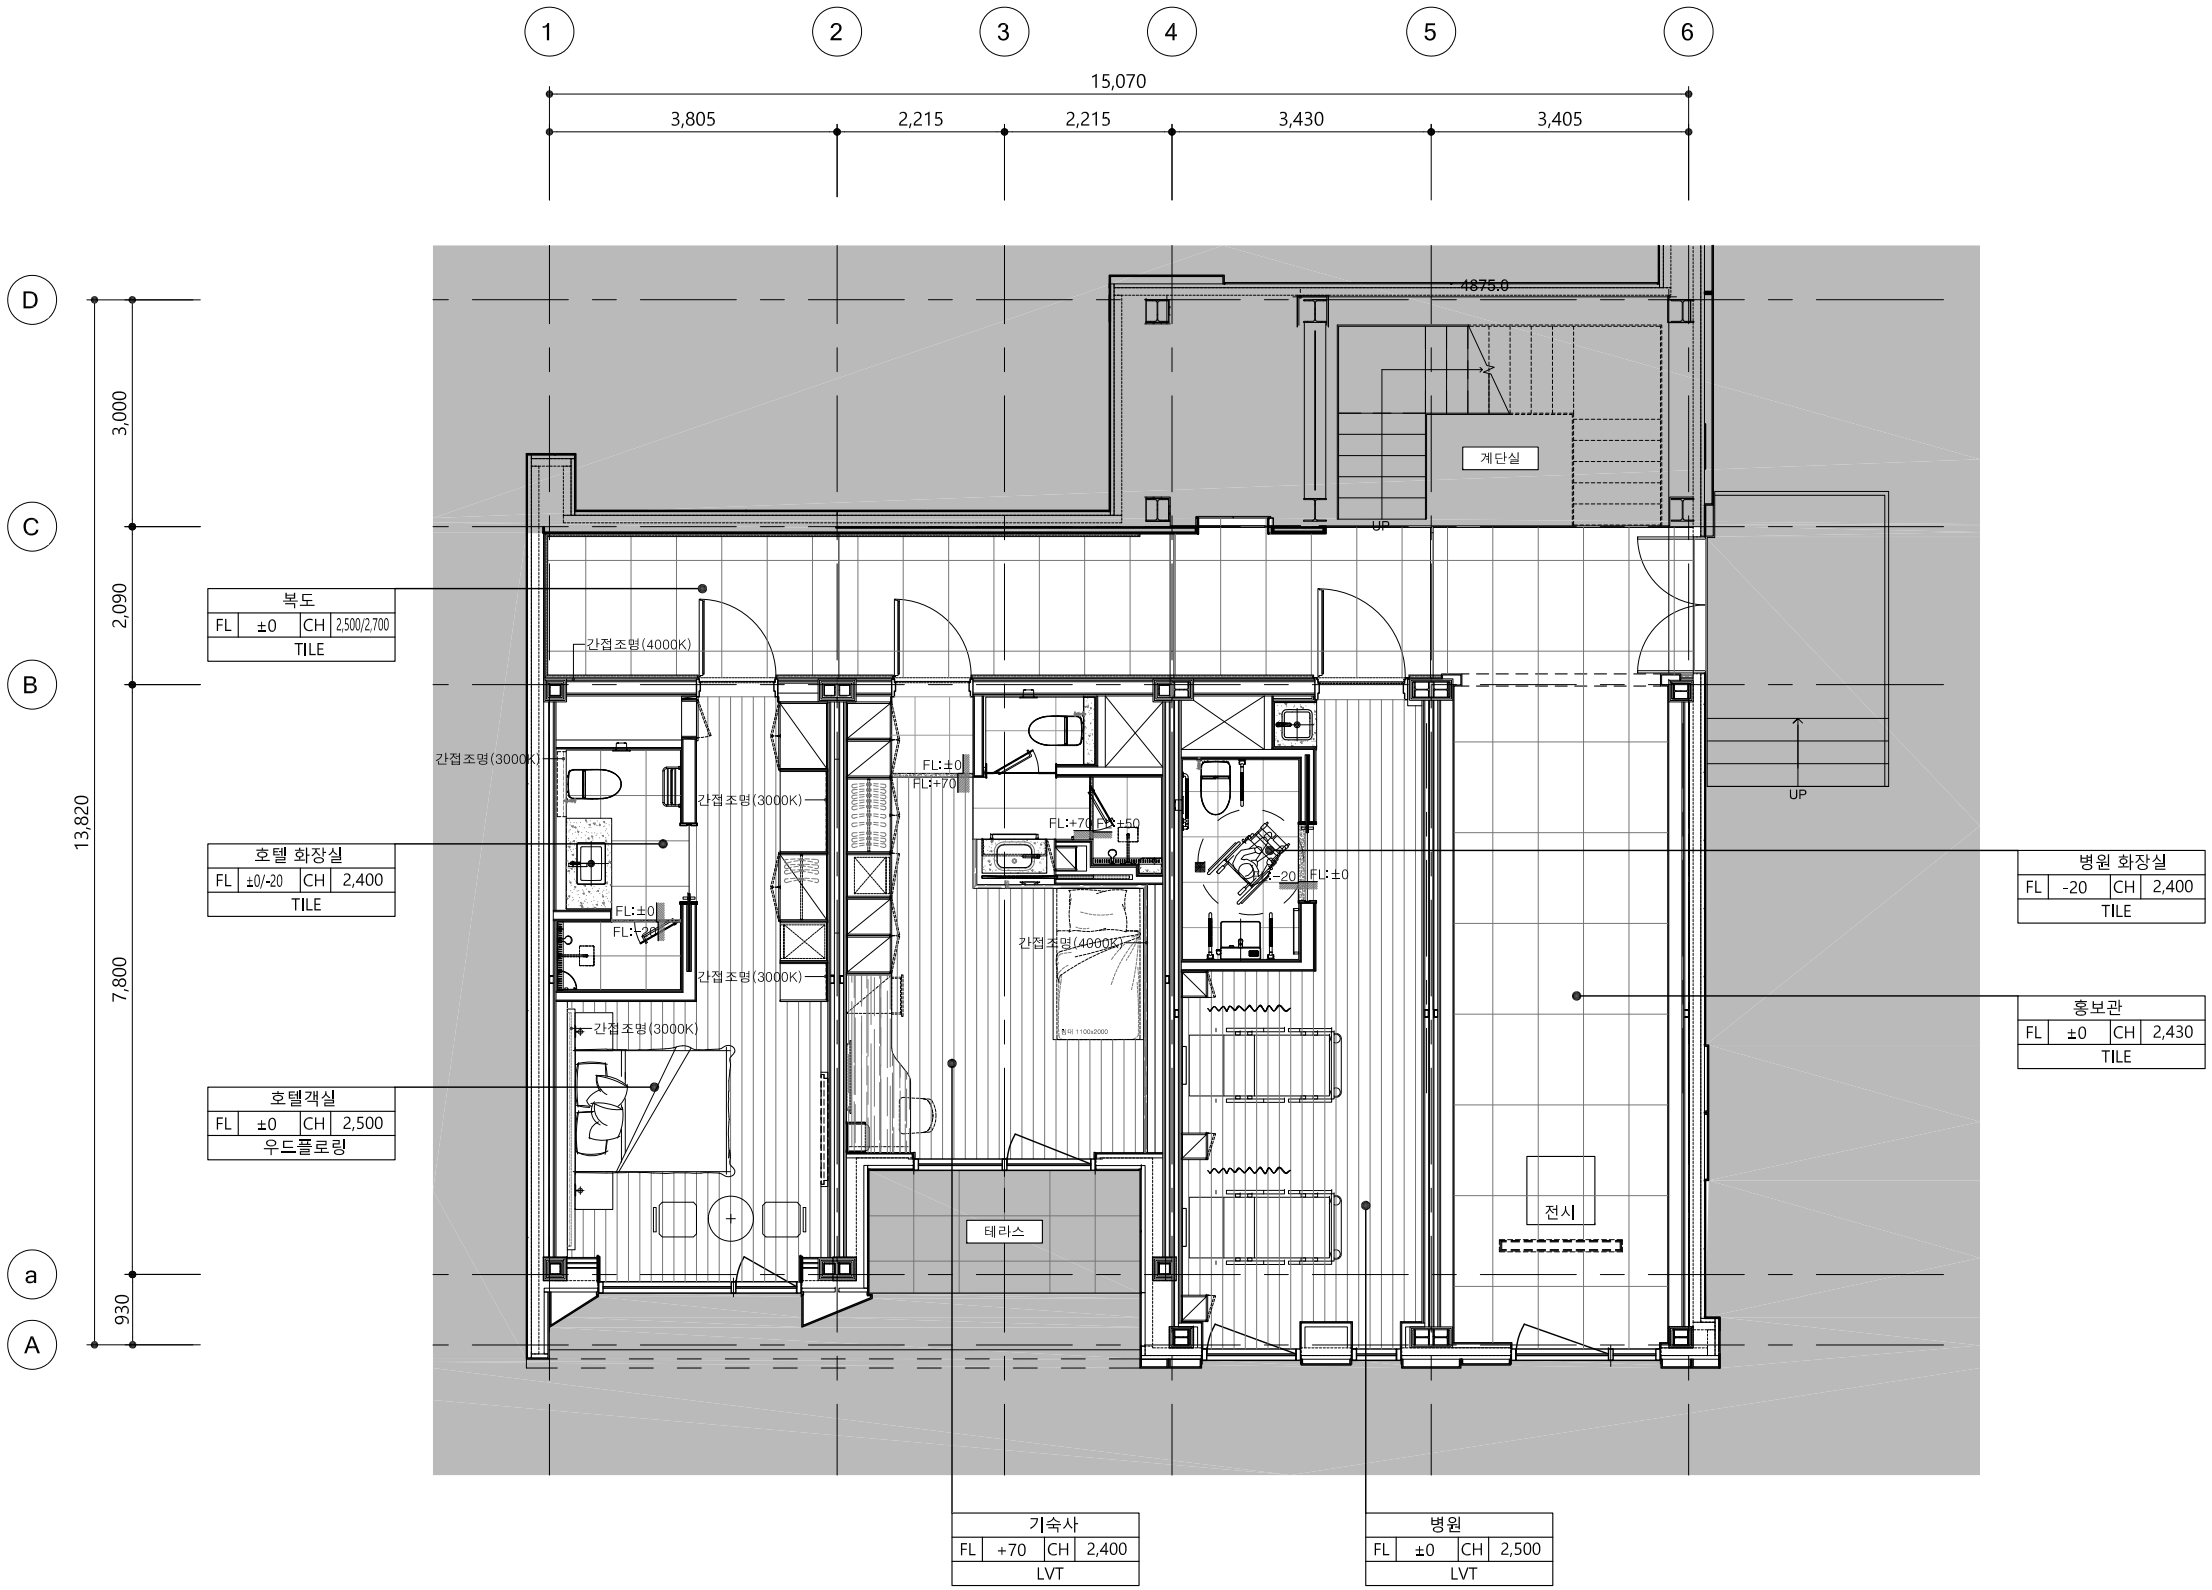



1 지상1층 평면도

SCALE
A1:1/50, A3:1/100

PROJECT TITLE

현대엔지니어링
모듈러주택 테스트베드
인테리어 설계

NOTE

인테리어 영역
건축영역

FORTE
ARCHITECTURE & INTERIOR

33-1, Bongeunsa-ro 68-gil FORTE B/D
GANGNAM-GU SEOUL, KOREA

DATE 2024.10.

APPROVE

CHECKED BY

DRAWN BY

SCALE A1 1 / 50
A3 1 / 100

DRAWING TITLE

지상1층 평면도

SHEET NO.

004

DRAWING NO.

P-101