
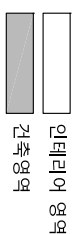
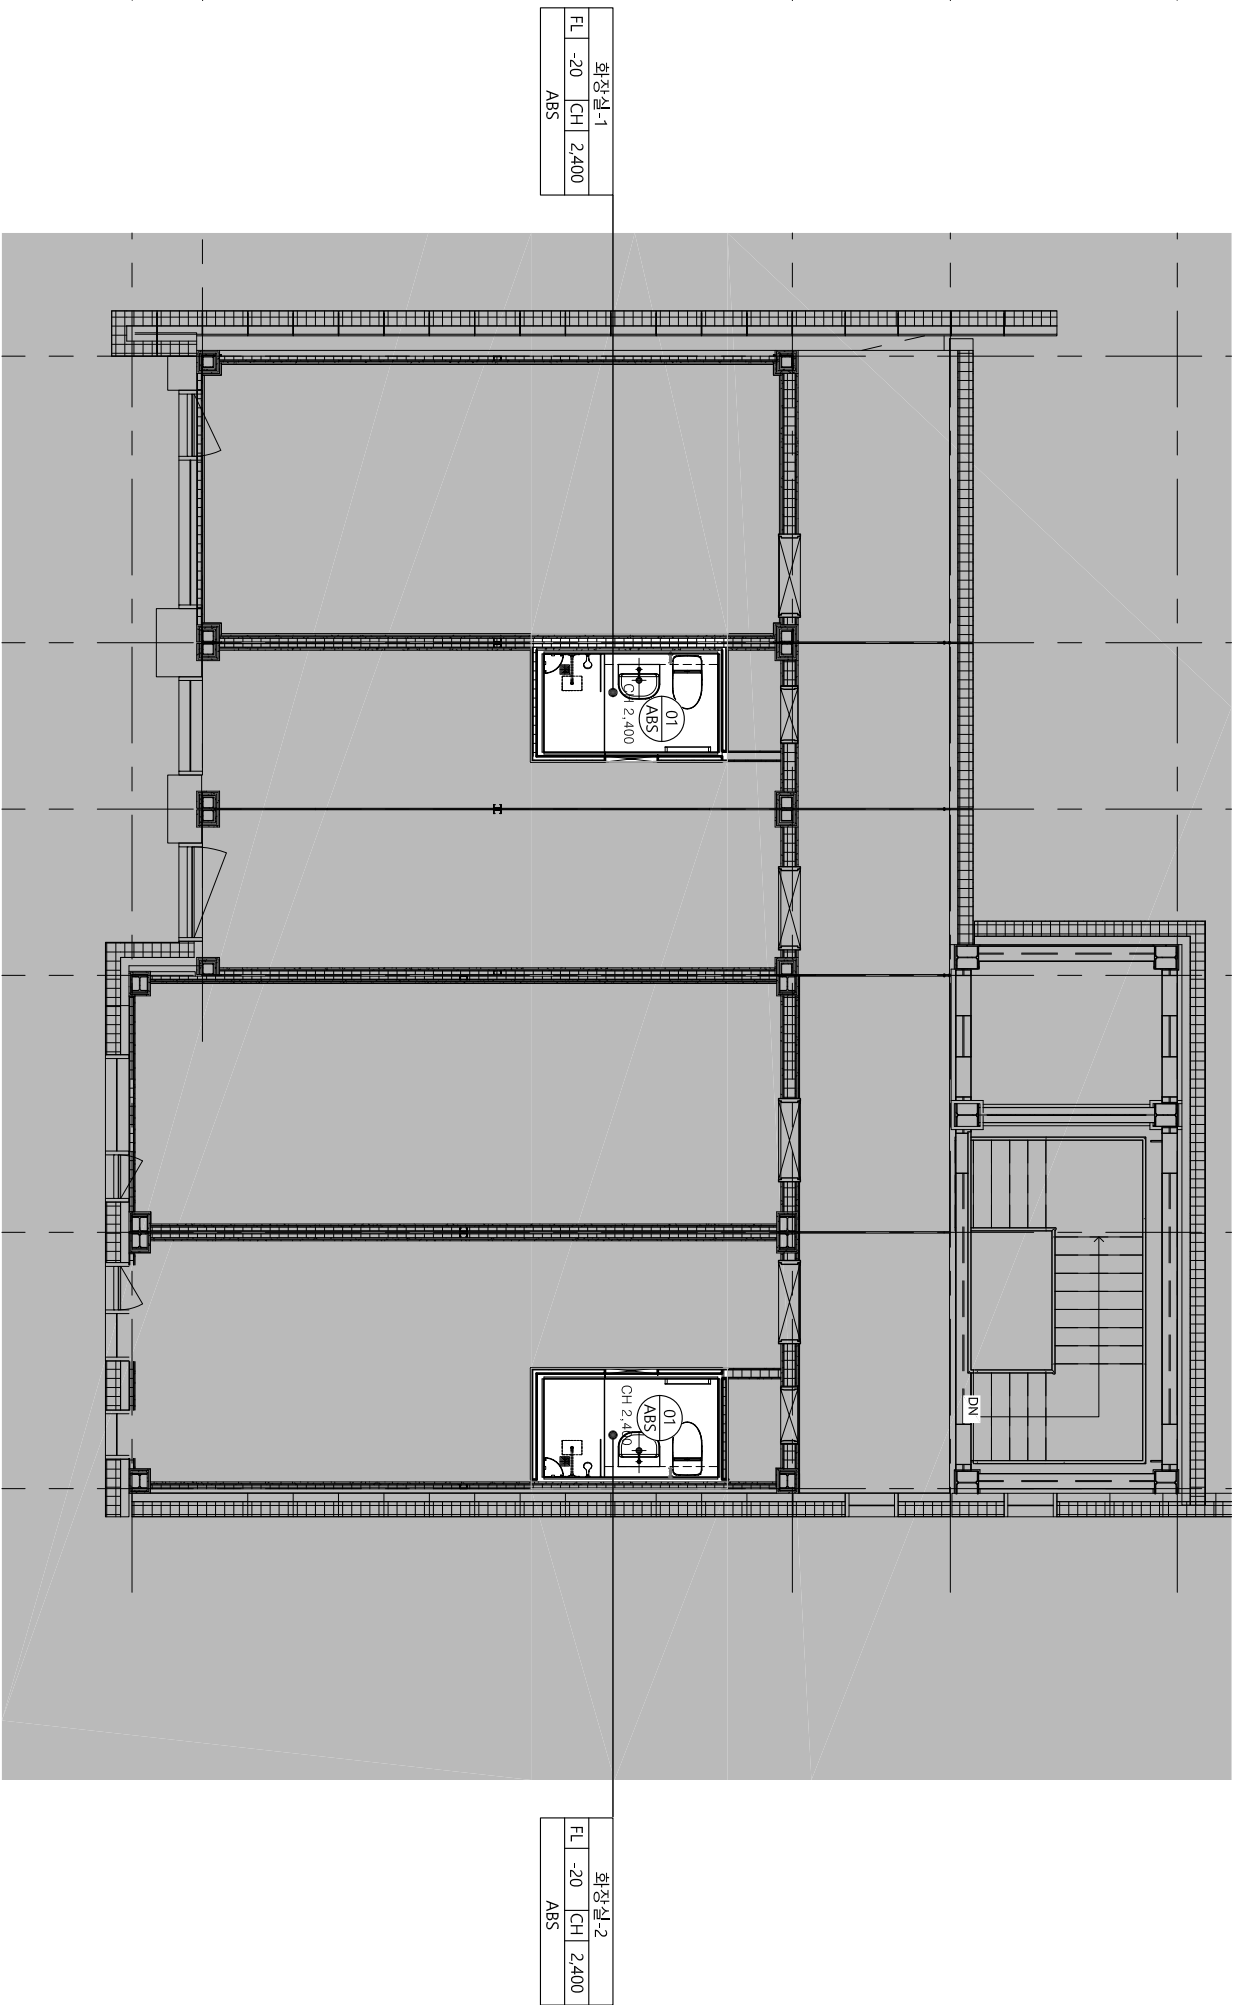
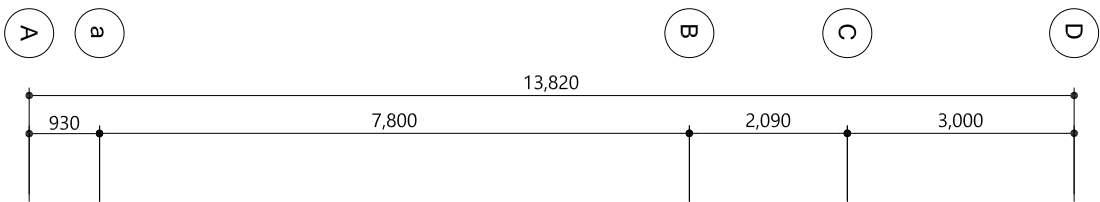


PROJECT TITLE

현대엔지니어링
모듈러주택 테스트베드
인테리어 설계

NOTE

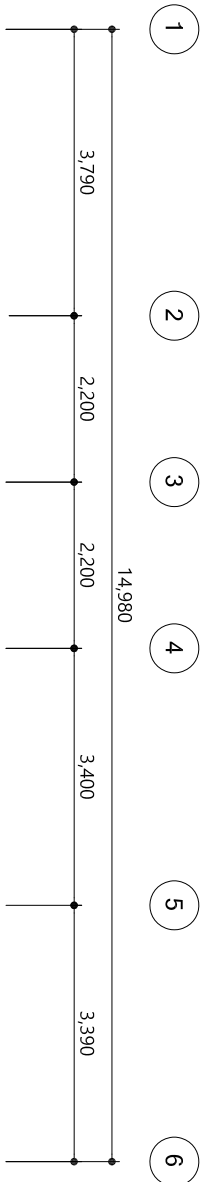

FORTE
ARCHITECTURE & INTERIOR

33-1, Bongseunsa-ro 68-gil FORTE B/D
GANGNAM-GU SEOUL, KOREA

DATE 2024.10.

APPROVE

CHECKED BY

DRAWN BY

SCALE	A1	1 / 50
	A3	1 / 100

DRAWING TITLE

지상2층 천장도

SHEET NO.

009

DRAWING NO.

P-106

1 지상2층 천장도

SCALE

A1:1/50, A3:1/100