
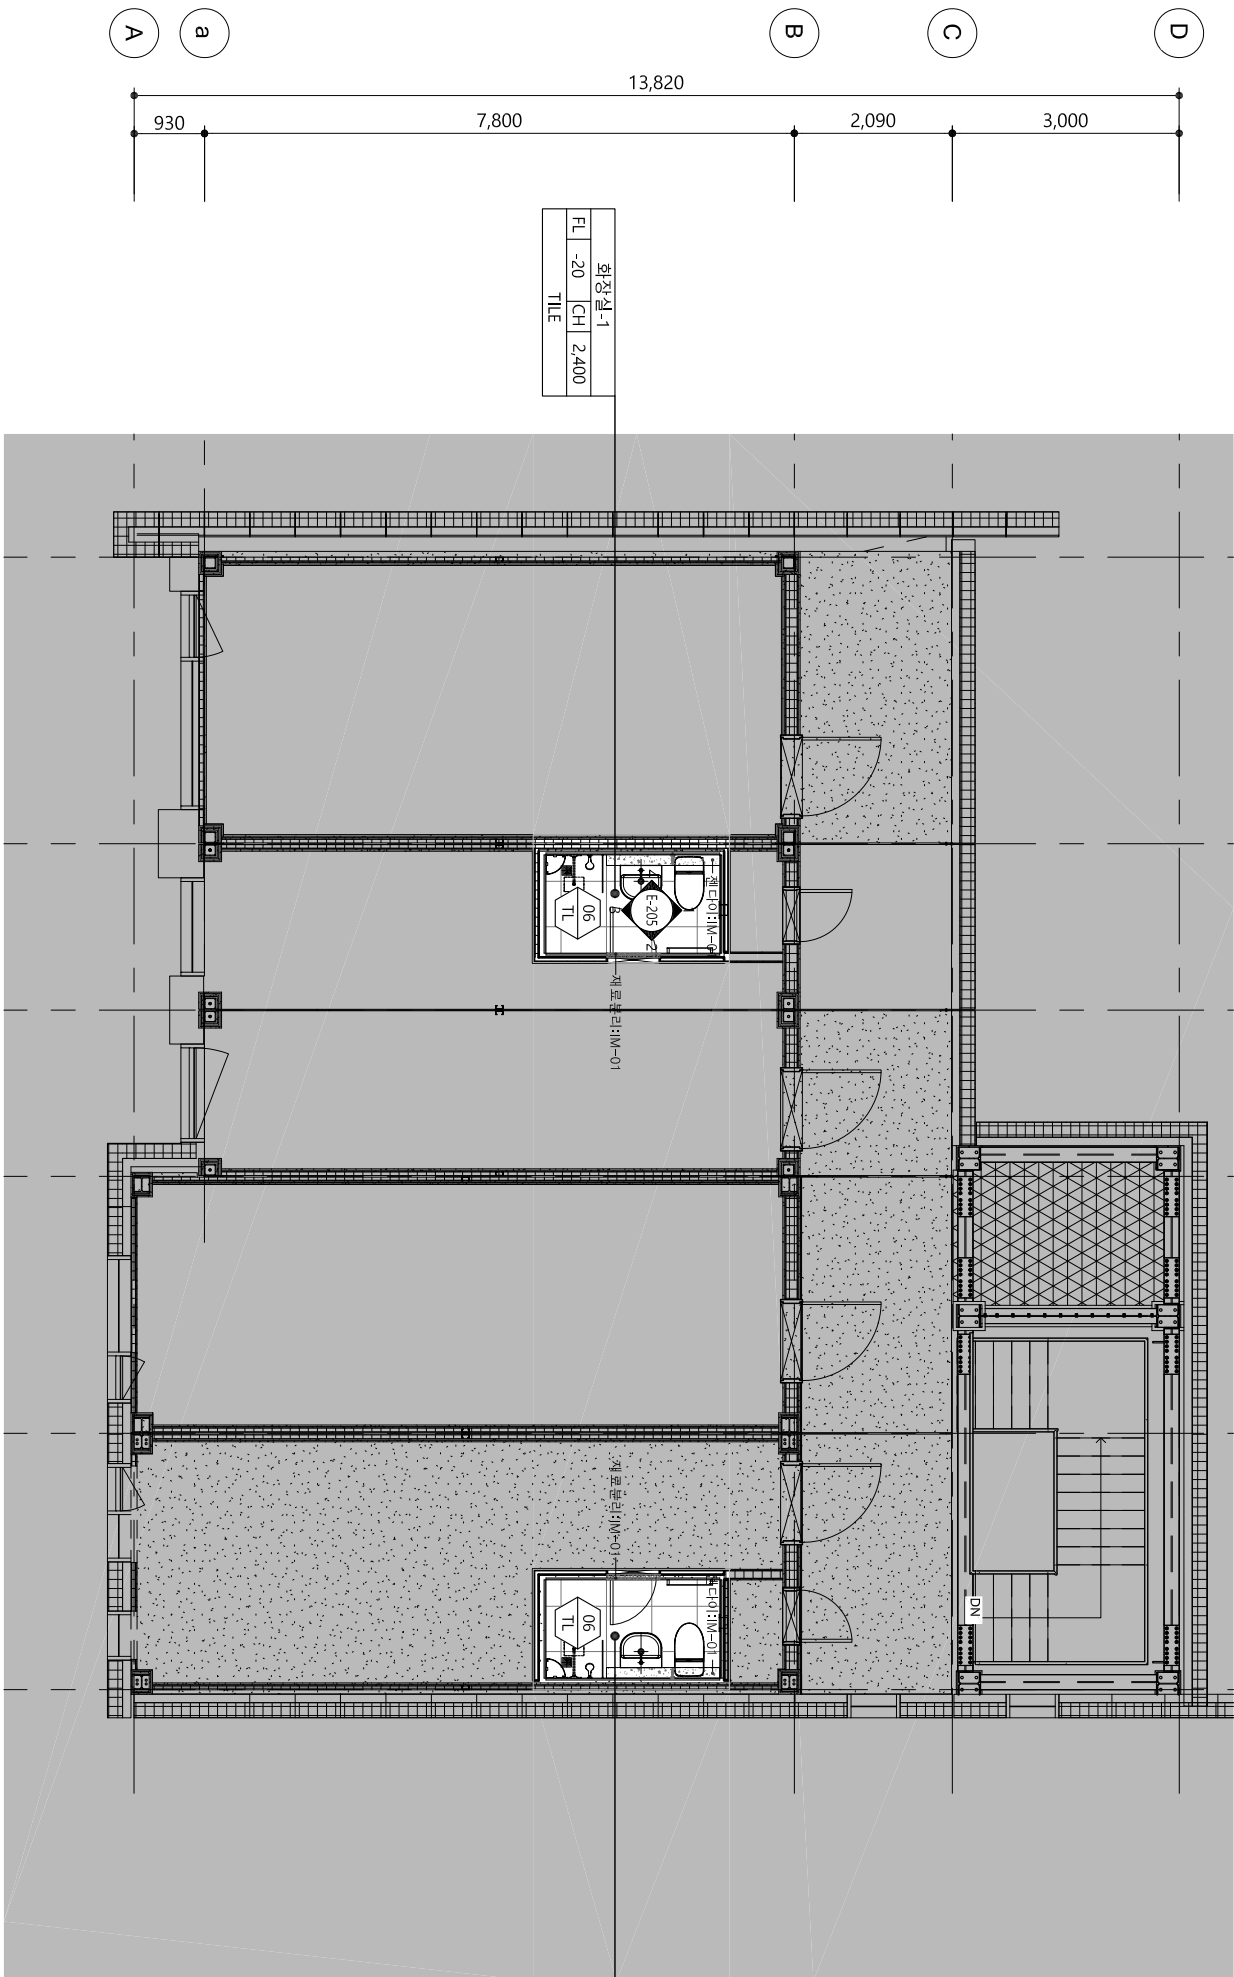


PROJECT TITLE

현대엔지니어링
모듈러주택 테스트베드
인테리어 설계

NOTE

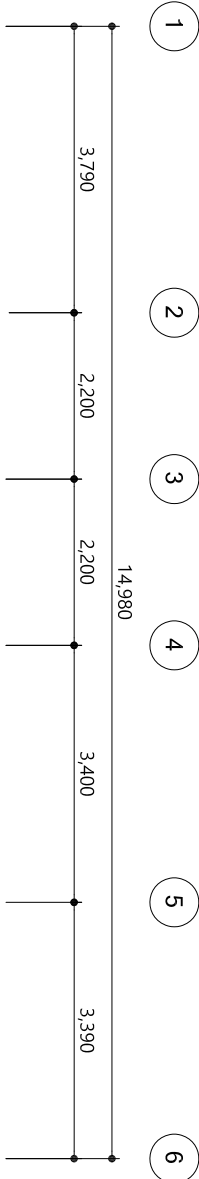

화장실-1		
FL	-20	CH 2,400
TILE		

화장실-2		
FL	-20	CH 2,400
TILE		

- 인테리어 영역
- 건축영역

FORTE
ARCHITECTURE & INTERIOR

33-1, Bongseunsa-ro 68-gil FORTE B/D
GANGNAM-GU SEOUL, KOREA

DATE 2024.10.

APPROVE

CHECKED BY

DRAWN BY

SCALE	A1	1 / 50
	A3	1 / 100

DRAWING TITLE

지상2층 평면도

SHEET NO.

008

DRAWING NO.

P-105

SCALE

A1:1/50, A3:1/100

1 지상2층 평면도,