



NOTE

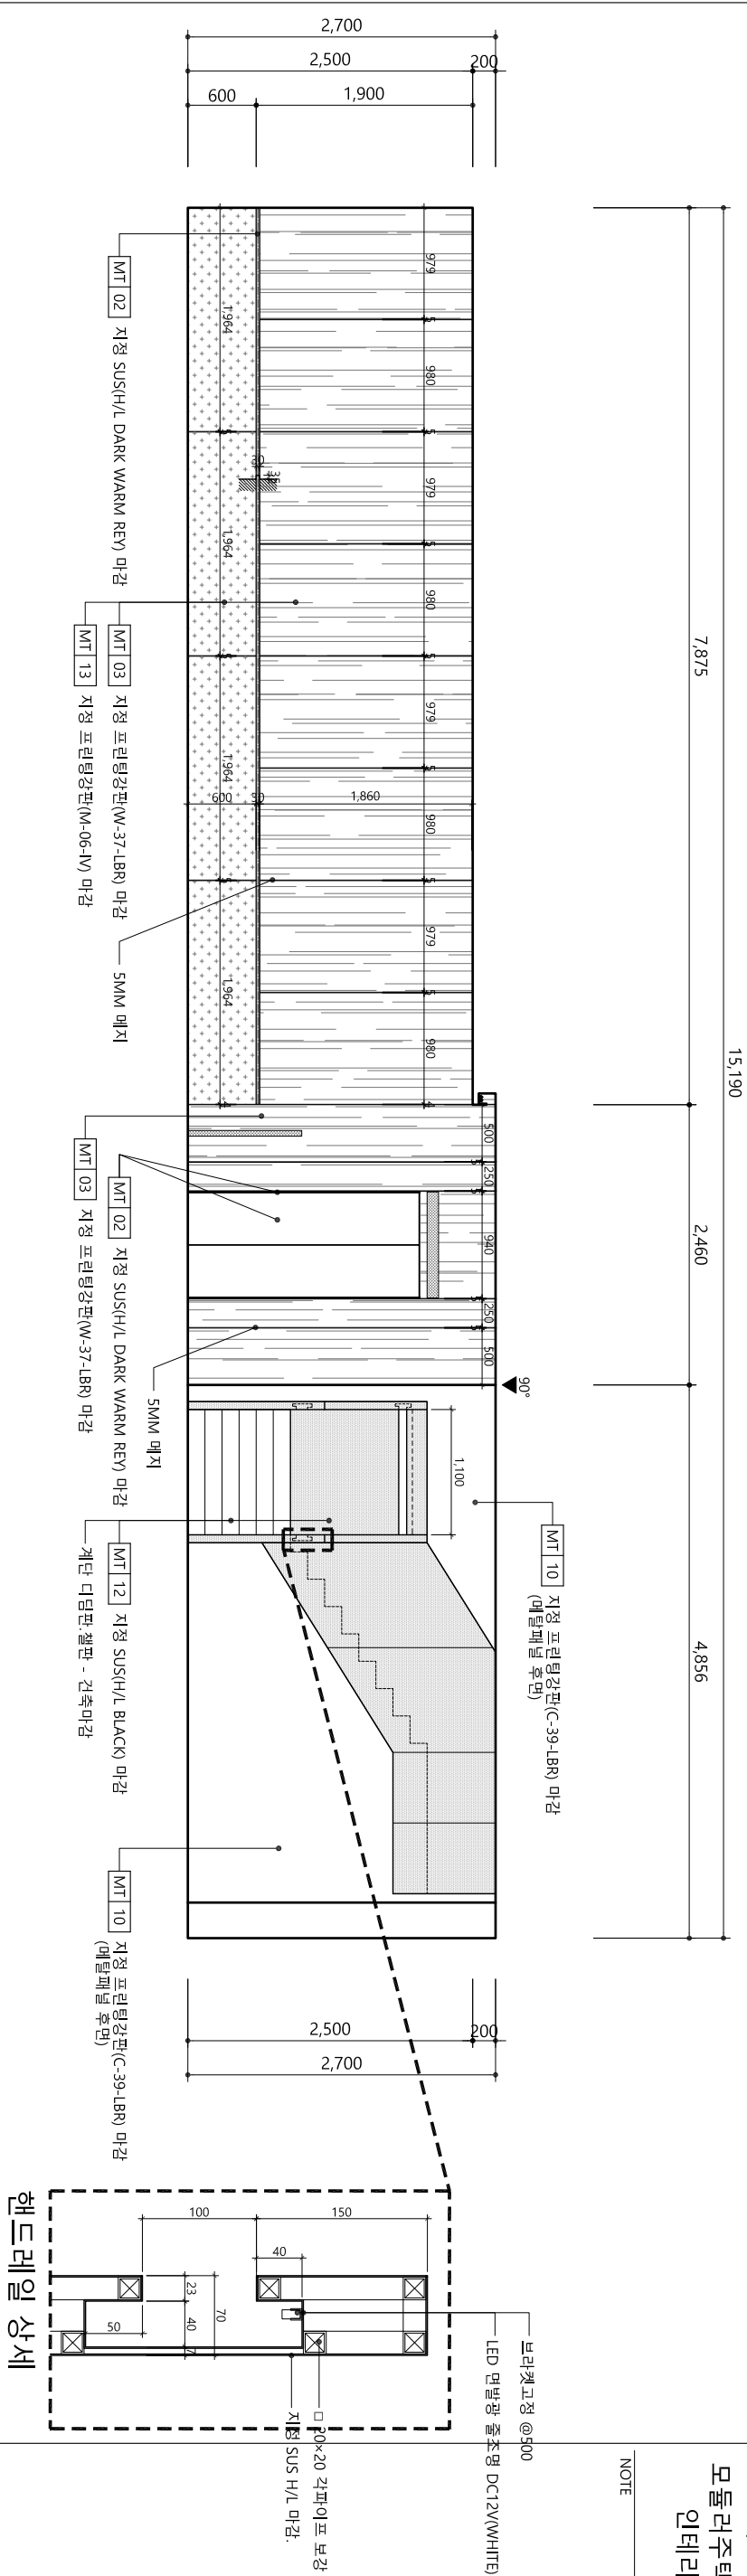


1 지상 1층 복도 입면도 -1

SCALE
A1:1/30, A3:1/60

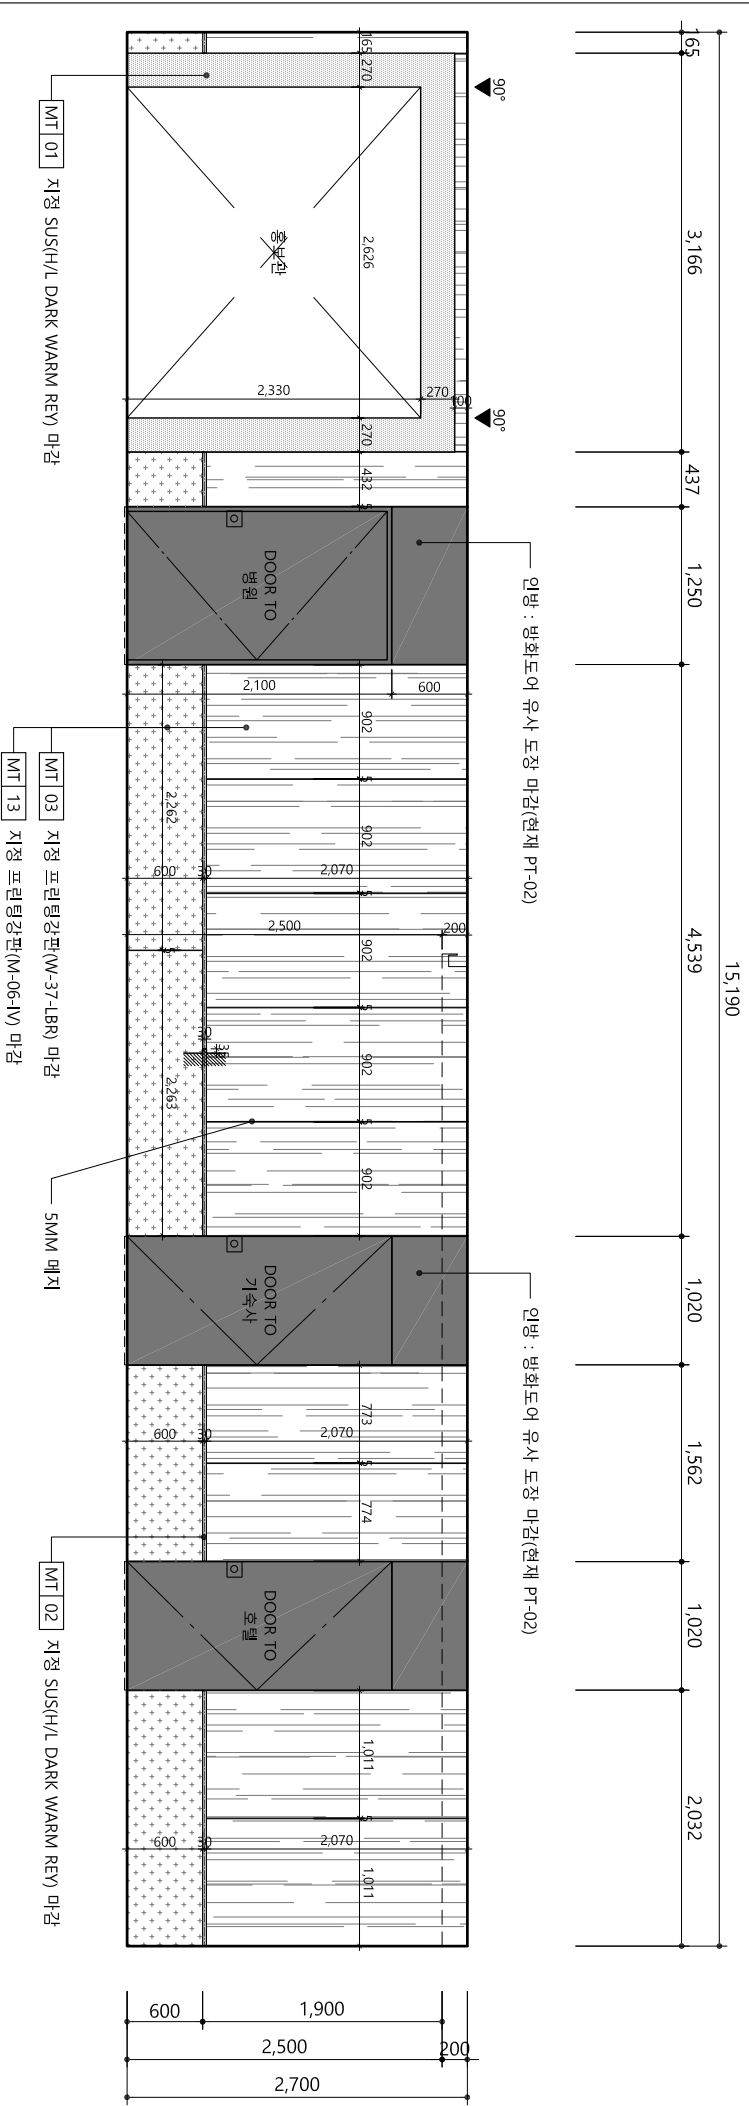

2 지상 1층 복도 입면도 -2

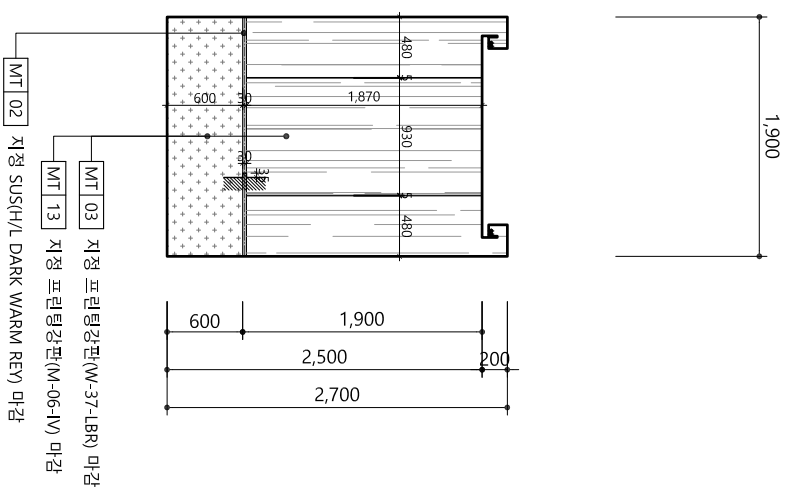

3 지상 1층 복도 입면도 -3

FORTE
ARCHITECTURE & INTERIOR

33-1, Bongseunsa-ro 68-gil, FORTE B/D
GANGNAM-GU SEOUL, KOREA

DATE 2024.10.

APPROVE

CHECKED BY

DRAWN BY

SCALE A1 1 / 30
A3 1 / 60

DRAWING TITLE

지상 1층
복도 입면도 -1

SHEET NO.

010

DRAWING NO.

E-101