
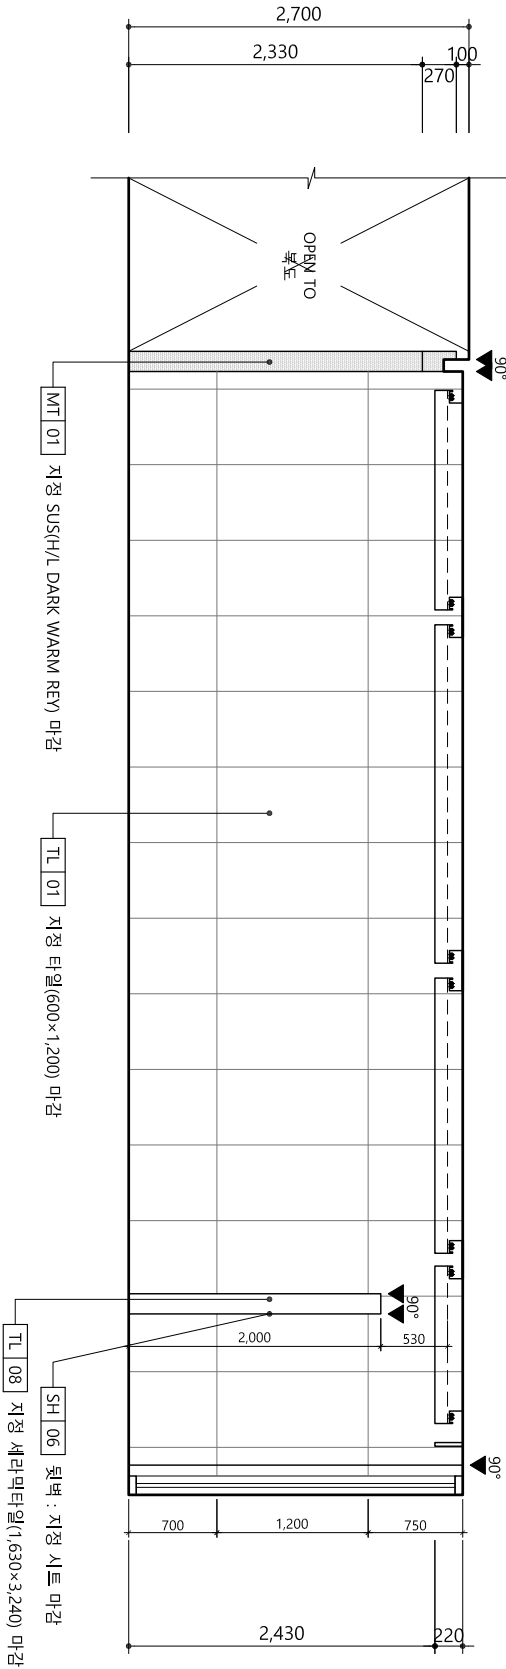
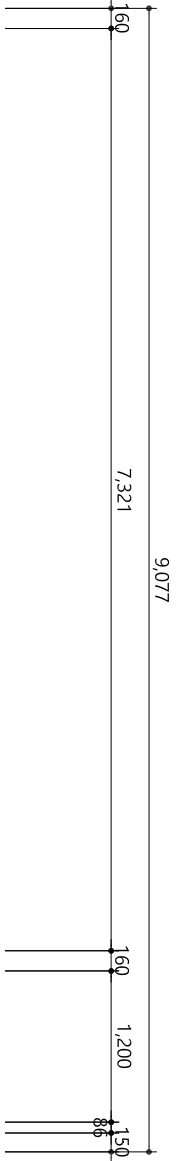
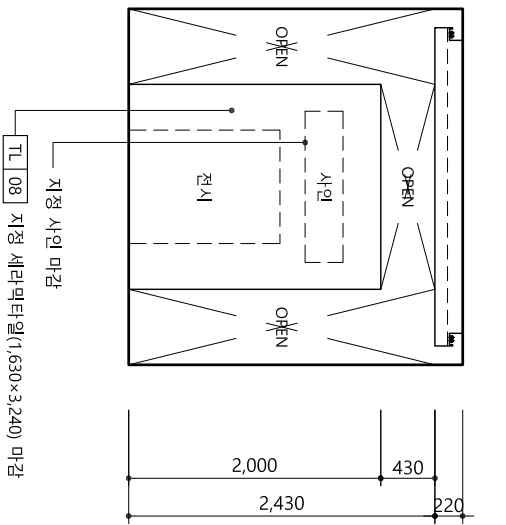


PROJECT TITLE

현대엔지니어링
모듈러주택 테스트베드
인테리어 설계

NOTE




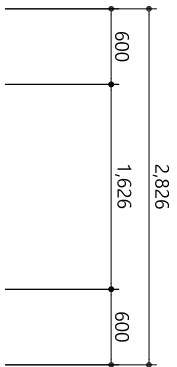


1 지상 1층 홍보관 입면도 -1

SCALE
A1:1/30, A3:1/60

2 지상 1층 홍보관 입면도 -2

SCALE
A1:1/30, A3:1/60

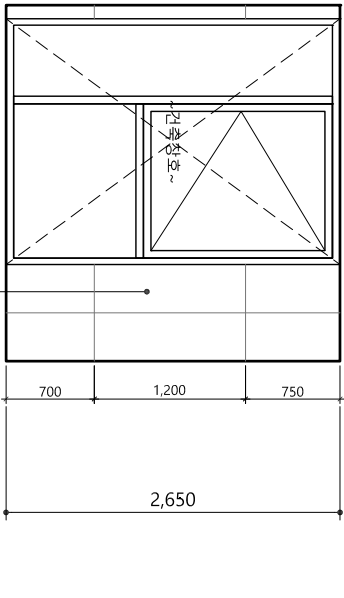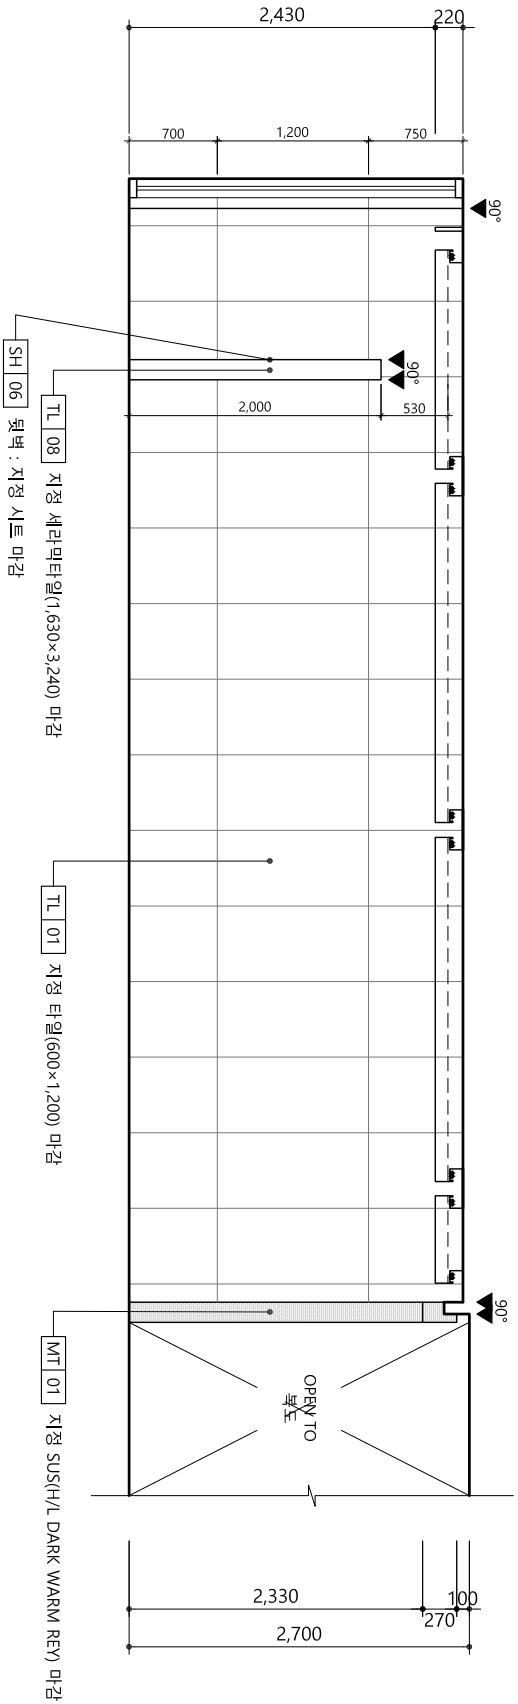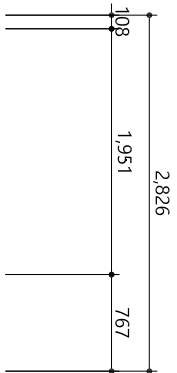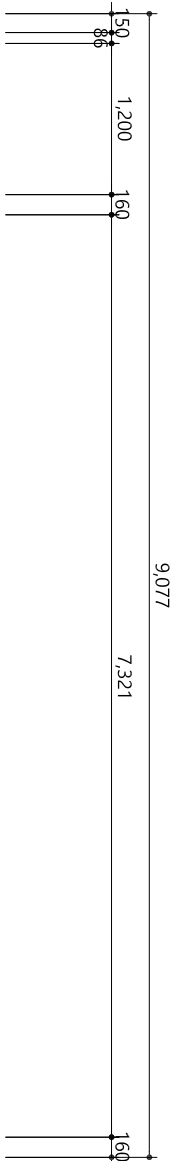

FORTE
ARCHITECTURE & INTERIOR

33-1, Bongseunsa-ro 68-gil FORTE B/D
GANGNAM-GU SEOUL, KOREA

DATE 2024.10.

APPROVE

CHECKED BY

DRAWN BY

SCALE	A1	1 / 30
	A3	1 / 60

DRAWING TITLE

지상 1층
홍보관
입면도 -1

SHEET NO.

011

DRAWING NO.

E-102

3 지상 1층 홍보관 입면도 -3

4 지상 1층 홍보관 입면도 -4

SCALE
A1:1/30, A3:1/60

SCALE
A1:1/30, A3:1/60