

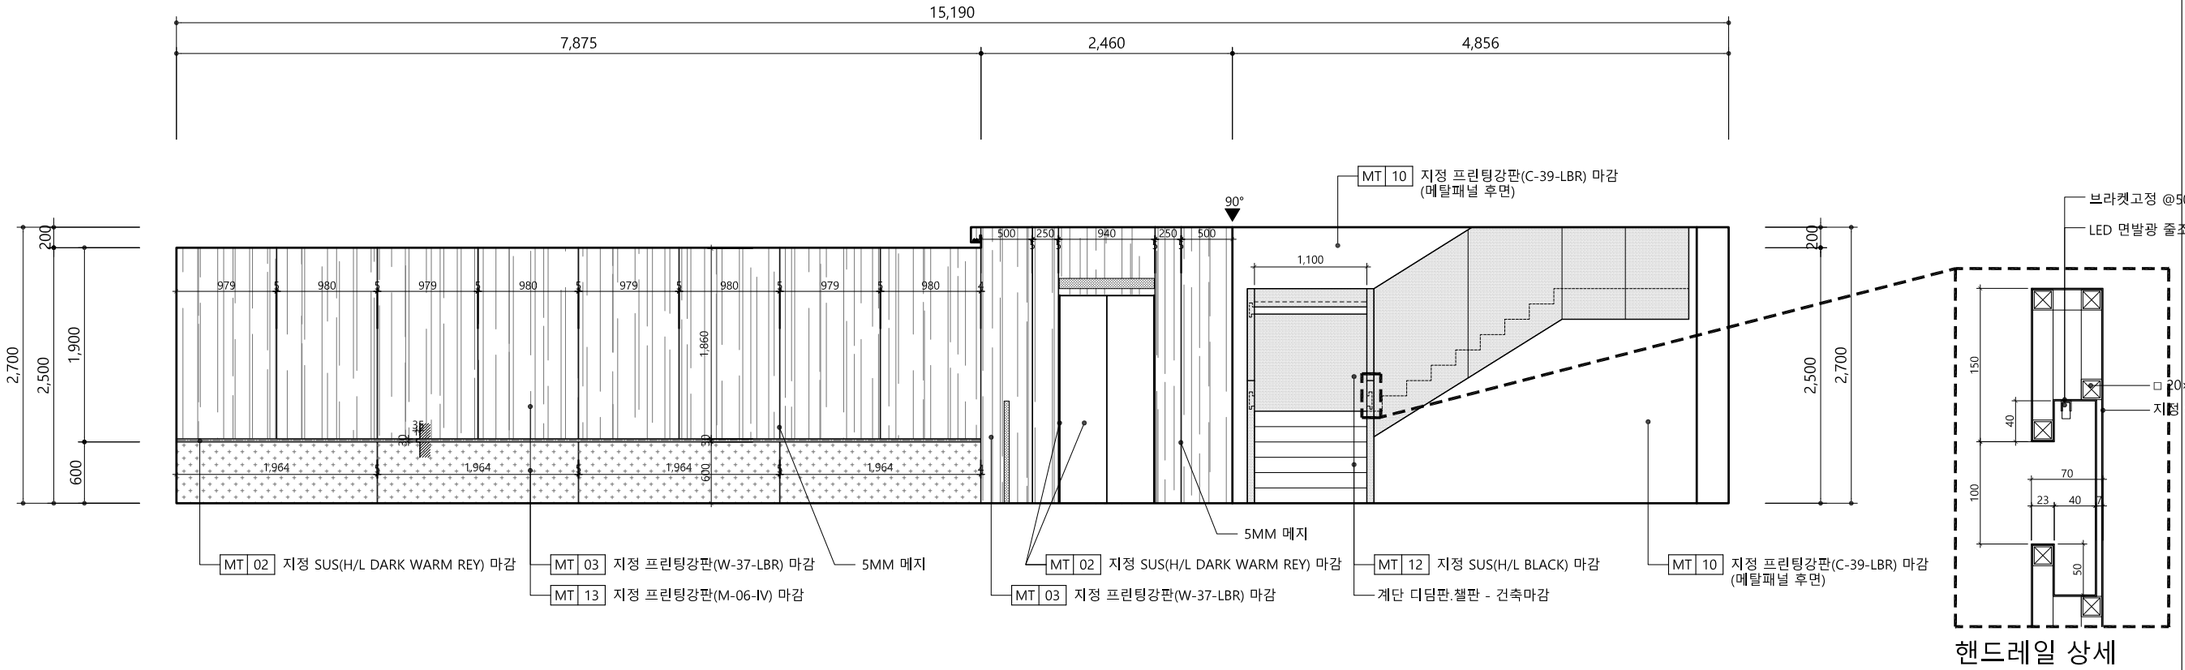


1 지상 1층 복도 입면도 -1

SCALE
A1:1/30, A3:1/60

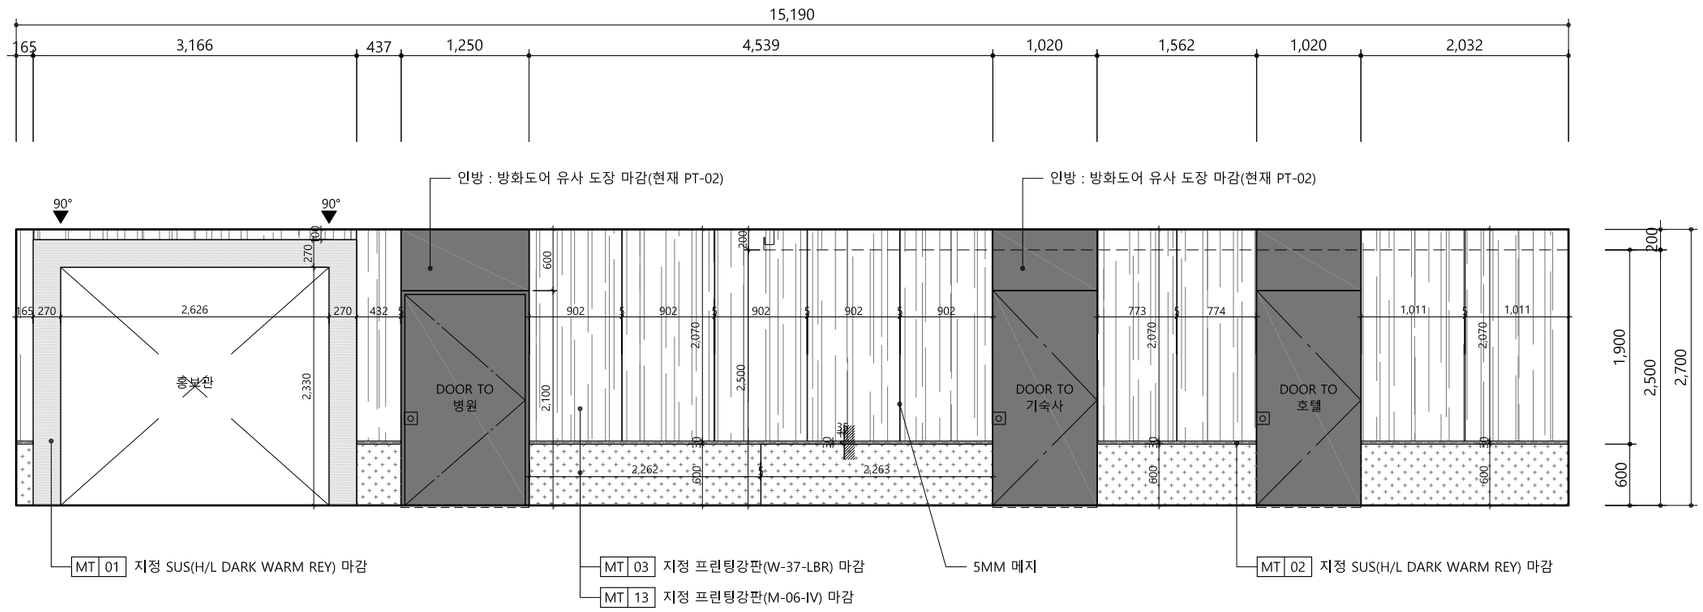

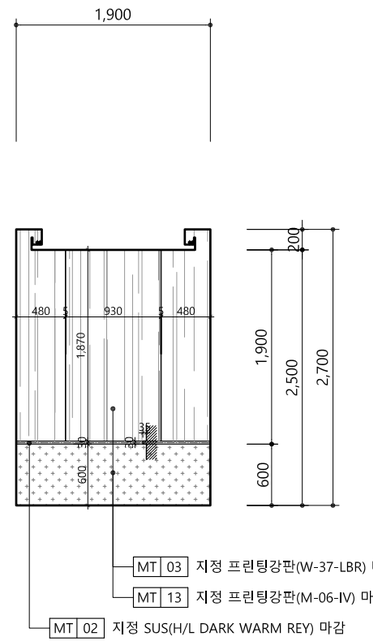

2 지상 1층 복도 입면도 -2

SCALE
A1:1/30, A3:1/60

3 지상 1층 복도 입면도 -3

PROJECT TITLE

현대엔지니어링
모듈러주택 테스트베드
인테리어 설계

NOTE

FORTE
ARCHITECTURE & INTERIOR
33-1, Bongeunsa-ro 68-gil FORTE B/D
GANGNAM-GU SEOUL, KOREA

DATE 2024.10.

APPROVE

CHECKED BY

DRAWN BY

SCALE A1 1 / 30
A3 1 / 60

DRAWING TITLE

지상 1층
복도 입면도 -1

SHEET NO.

010

DRAWING NO.

E-101